
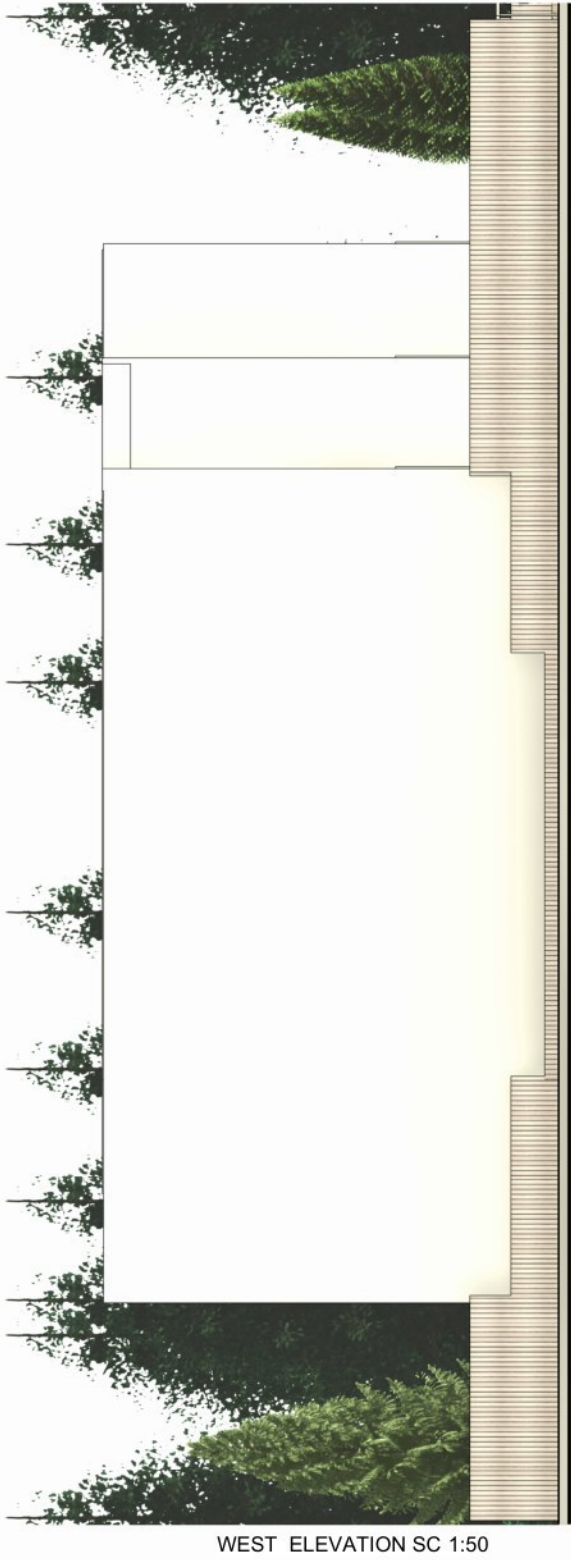


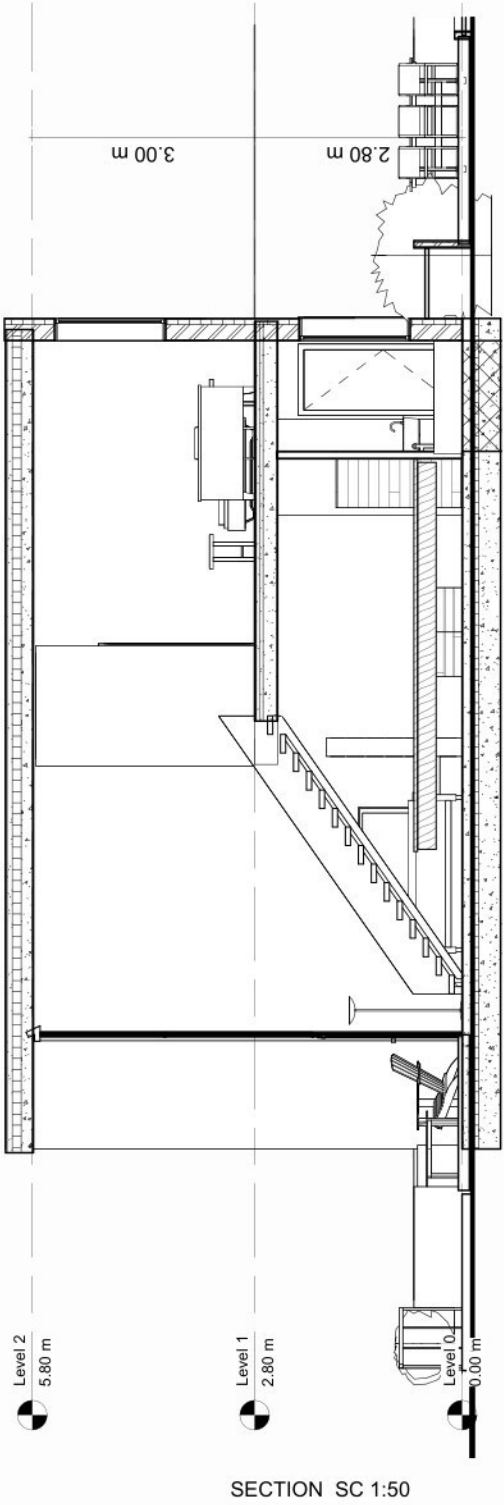


The project consists of a small residential development composed of three attached terraced houses. Each unit is designed as a compact duplex dwelling arranged over two floors, with a clear separation between the day area and the night area. The ground floor contains the main living spaces, including the living room, kitchen, and a bathroom, while the upper floor accommodates the bedroom area and an additional bathroom. This organization creates a simple and functional domestic layout, suitable for contemporary residential living.

A key architectural feature of the project is the use of large glazed façades and curtain-wall openings, which visually connect the interior spaces with the private outdoor areas. These glazed surfaces allow natural light to enter both the ground floor and the upper floor, improving the quality of the internal spaces and strengthening the relationship between the house and its garden. The outdoor areas are treated as extensions of the interior living spaces, with terraces, planters, vegetation, and private access paths contributing to a calm and comfortable residential atmosphere.

The project uses a clean and minimal material language. The main façade is finished with white plaster, giving the volume a simple and contemporary appearance. The exterior planters and fences introduce a warmer natural tone, balancing the clean white surfaces with a more domestic and tactile material expression. Dark-colored window and door frames define the openings and create a refined contrast with the light façade.

From a technical point of view, the building is represented through a BIM workflow using plans, elevations, sections, and construction details. The wall stratigraphy follows a layered construction system composed of exterior plaster, structural brick/block wall, exterior insulation, and interior plaster. The roof detail includes roof tiles, waterproofing, thermal insulation, screed for slope, concrete slab, and plaster. These elements demonstrate the integration between architectural design, material definition, and construction logic.

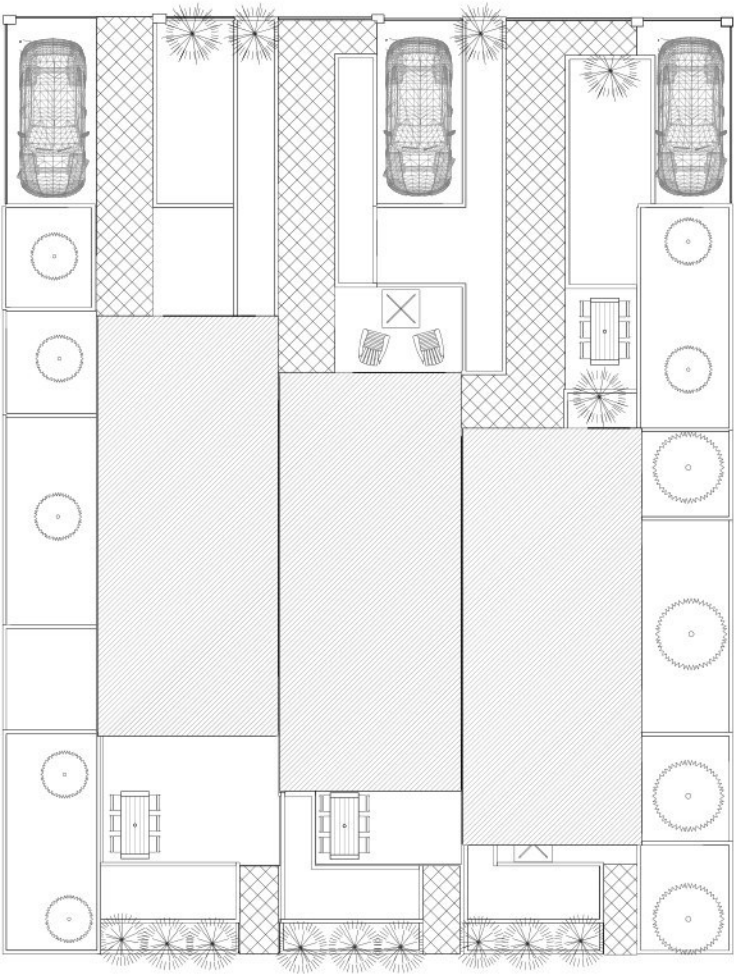

SITE PLAN SC 1:100

EAST ELEVATION SC 1:50






SOUTH ELEVATION SC 1:50



FIRST FLOOR PLAN SC 1:50



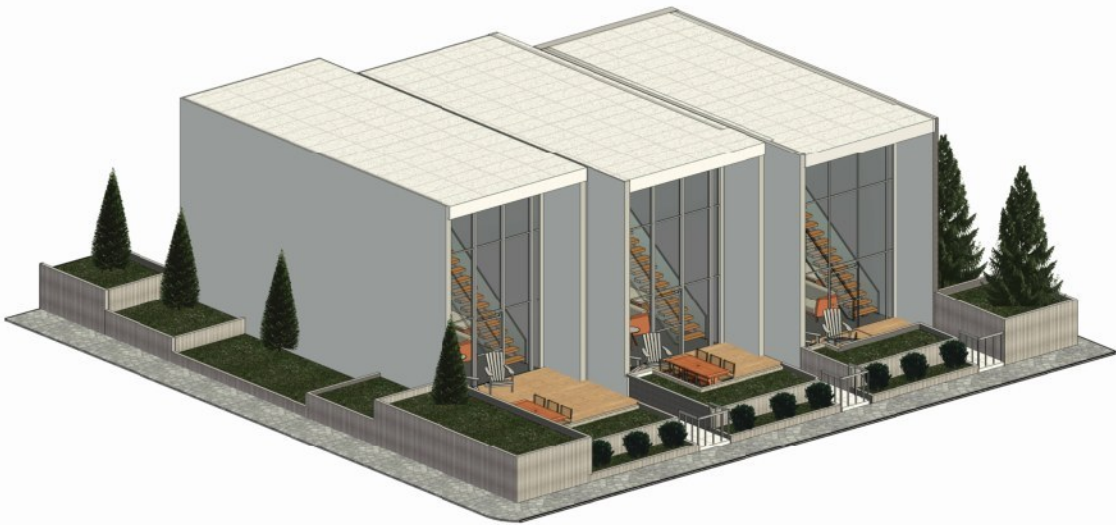


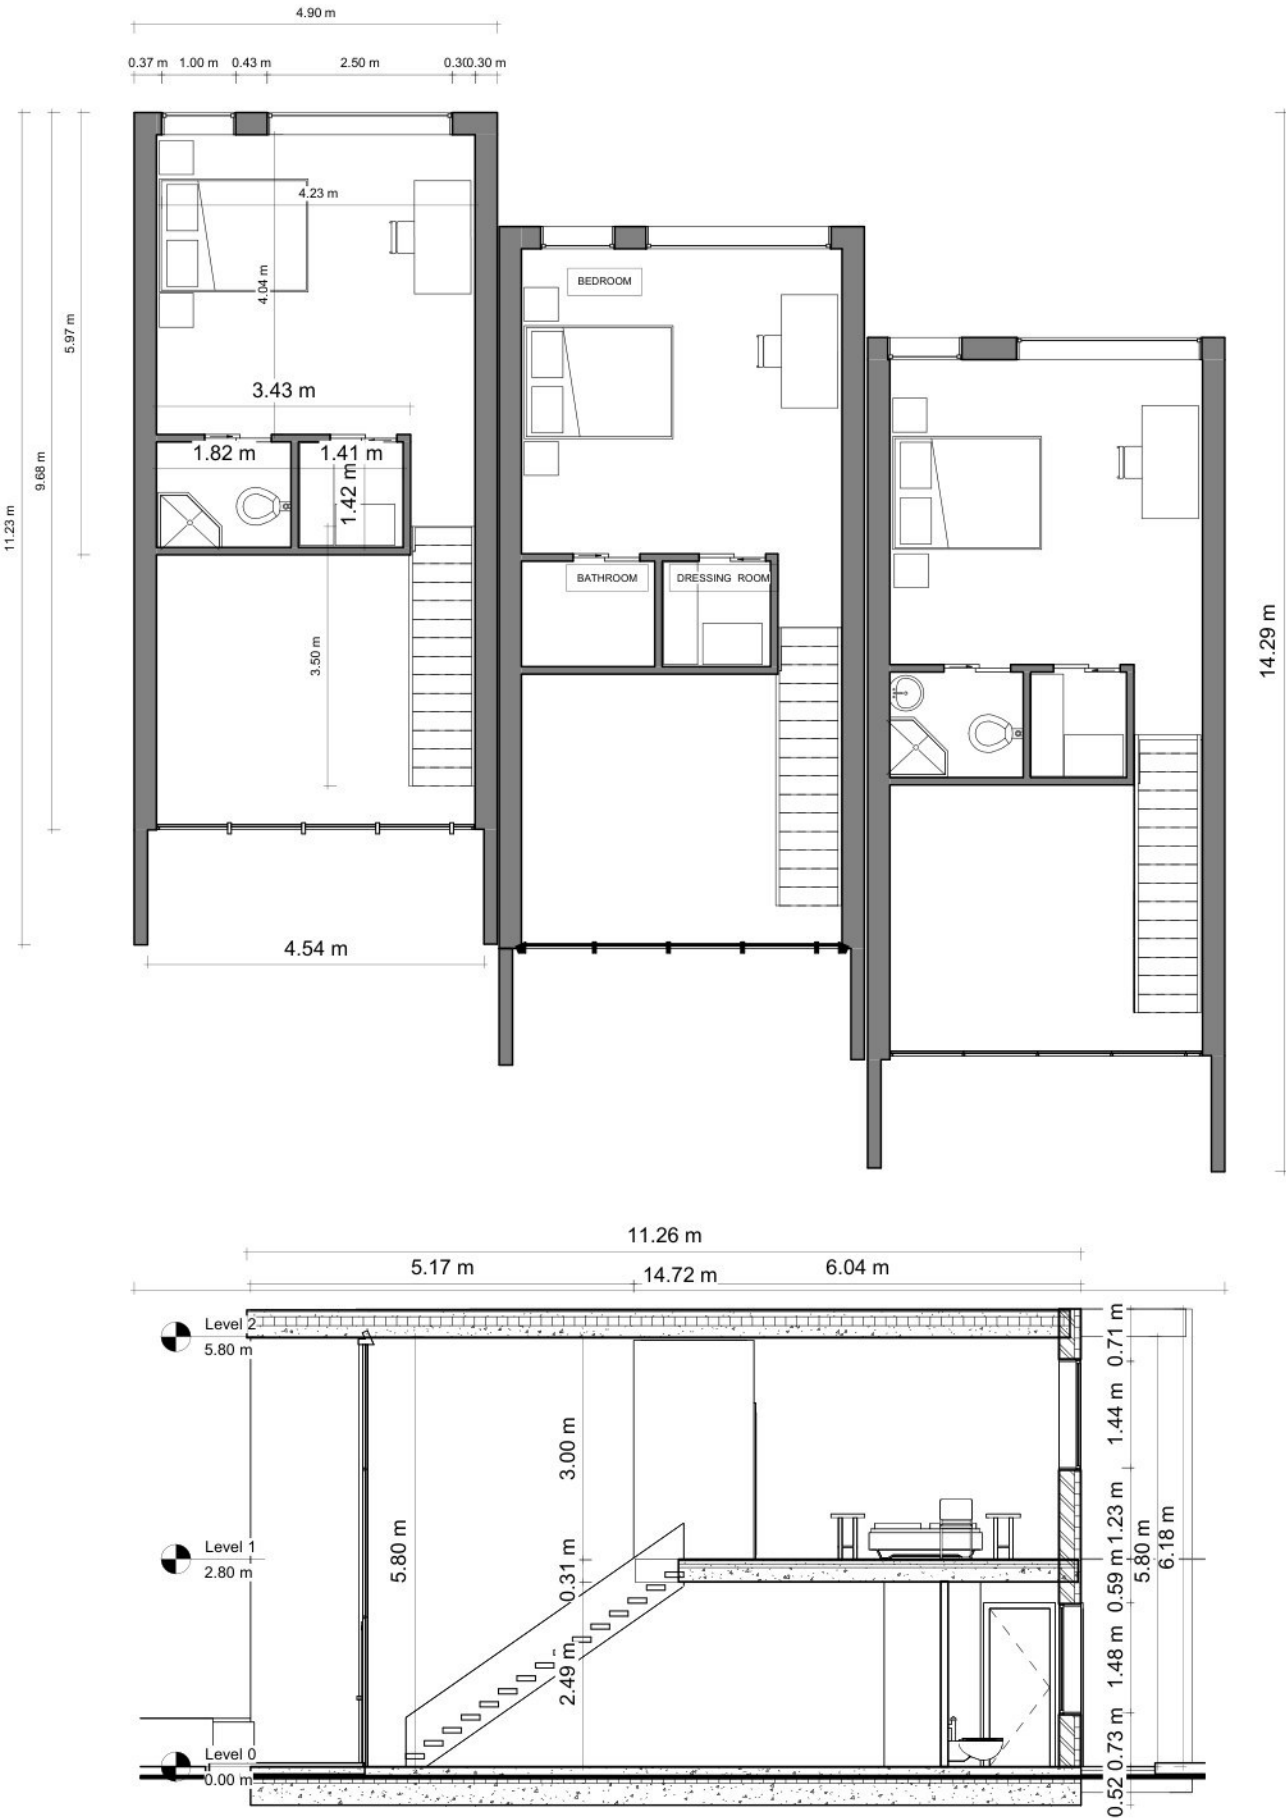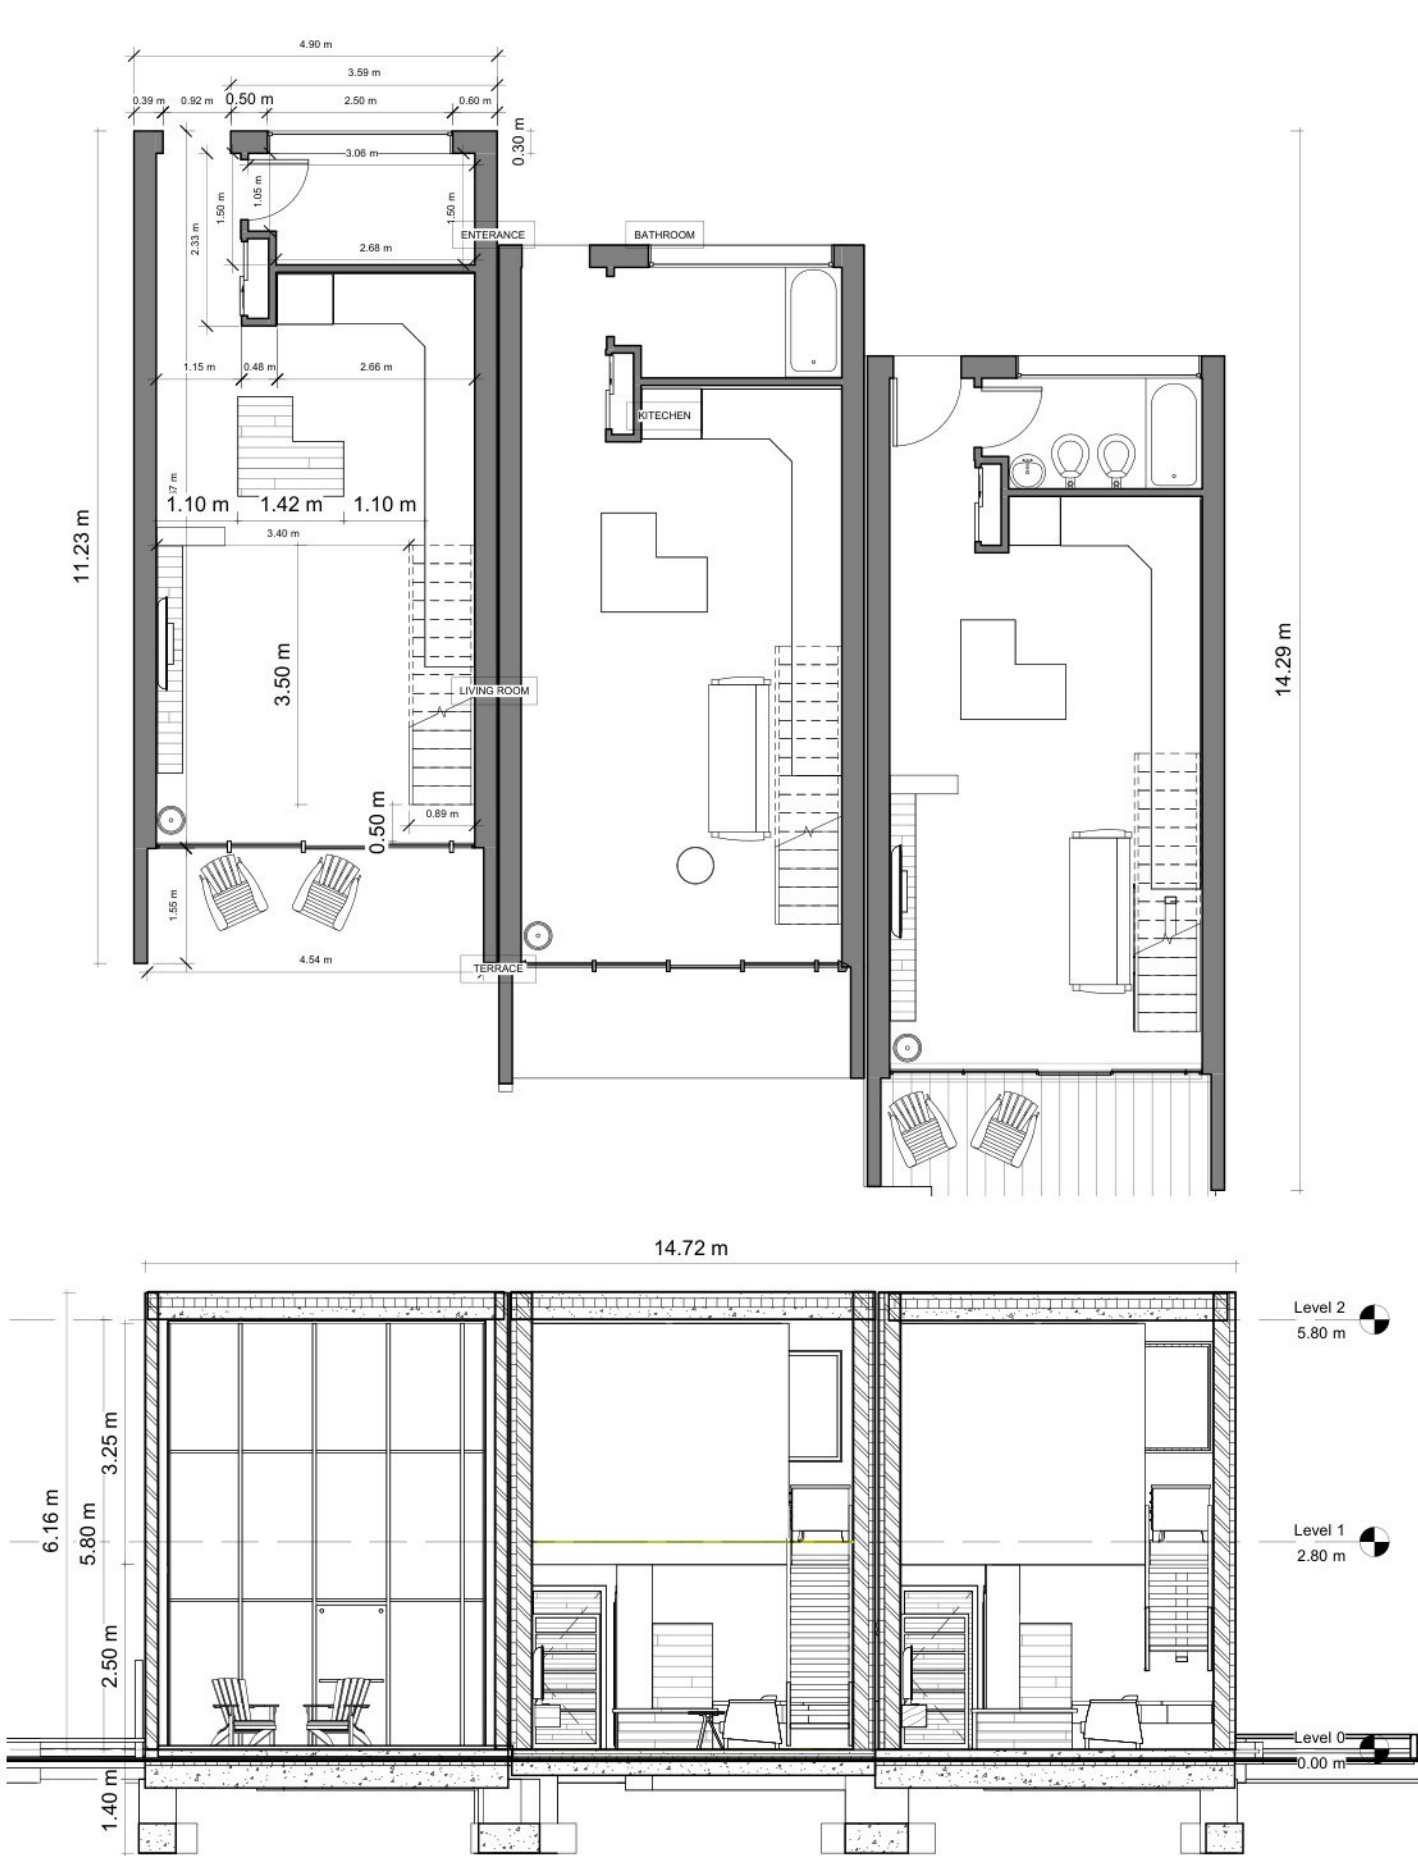





- | | | |
|--|---|--|
|  DARK THERMOWOOD FRAMING |  SILVER GREY STONE PAVING |  LUNA BEVEL HIDDEN NAILING DECK |
|  WHITE PLASTER |  THERMORY- LUNA ARCTIC THERMAL WOOD-GARDEN PLANTER |  GLASS |




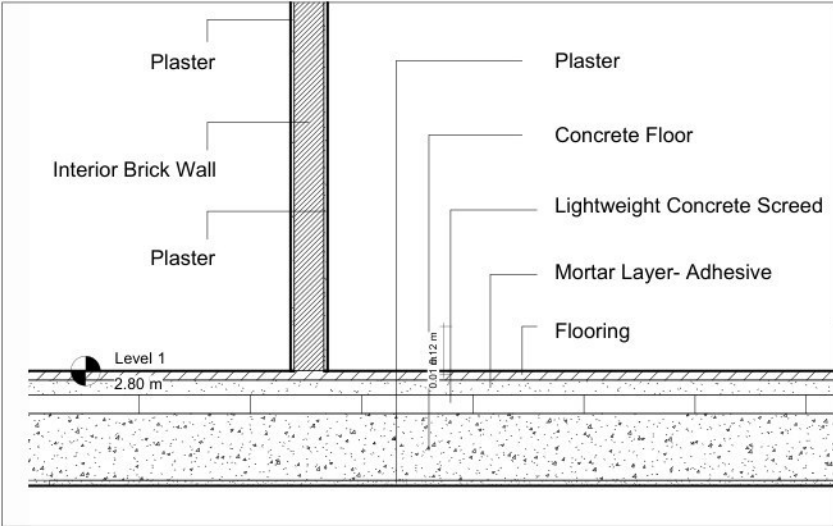


FIRST FLOOR DETAIL
INTERNAL WALL SECTION DETAIL

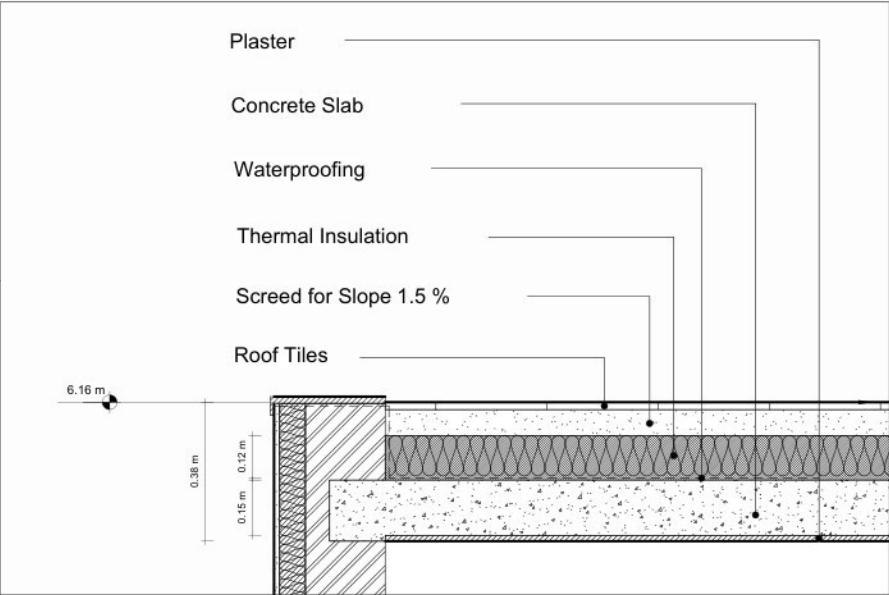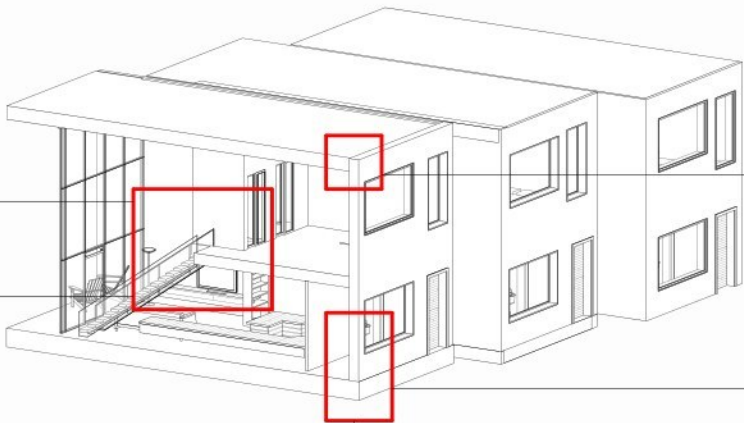


ROOF DETAIL STRATIGRAPHY

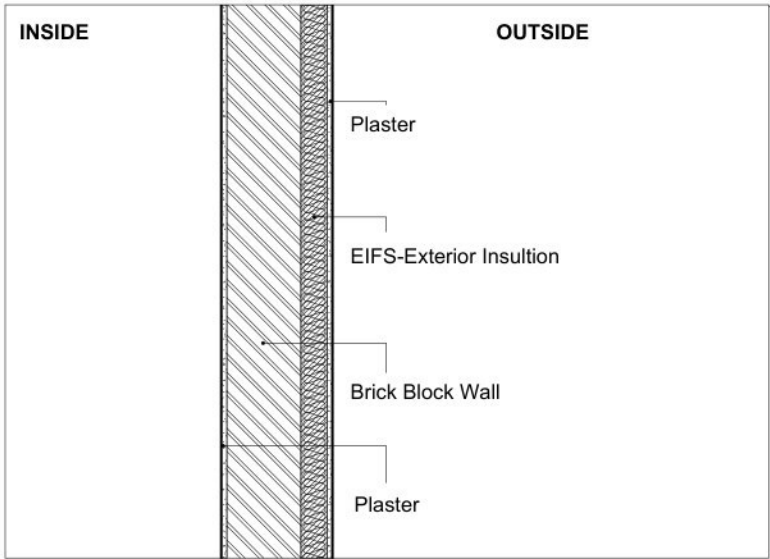

EXTERNAL WALL SECTION

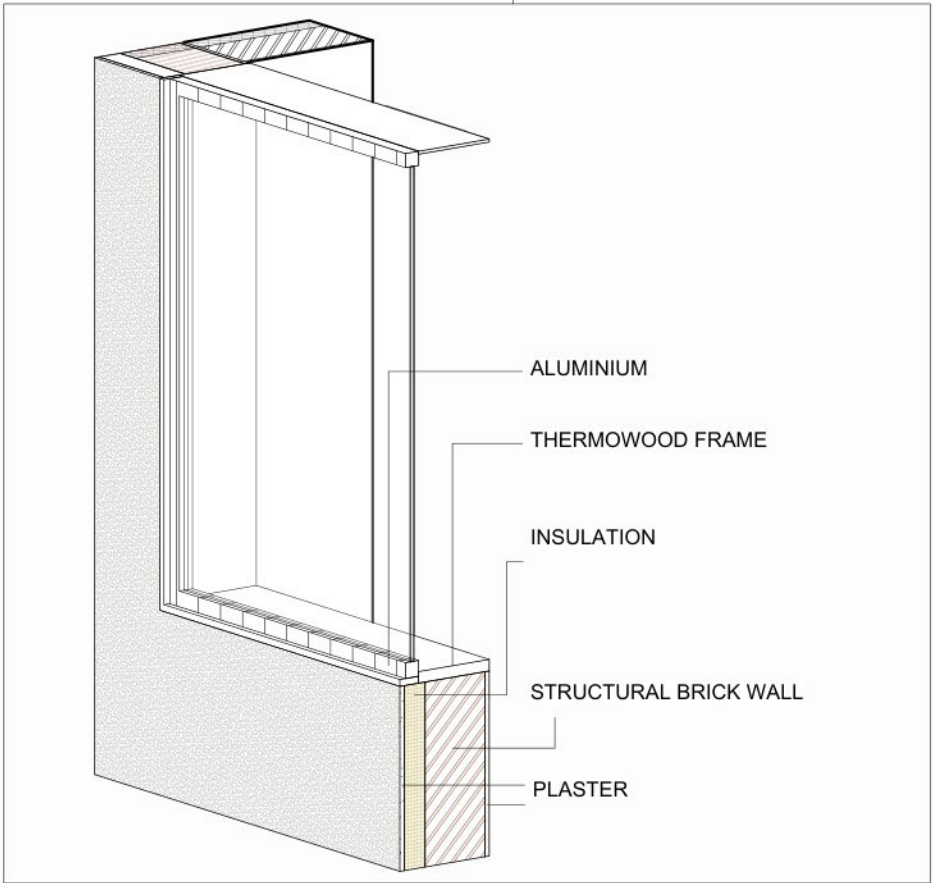

WINDOW DETAIL STRATIGRAPHY

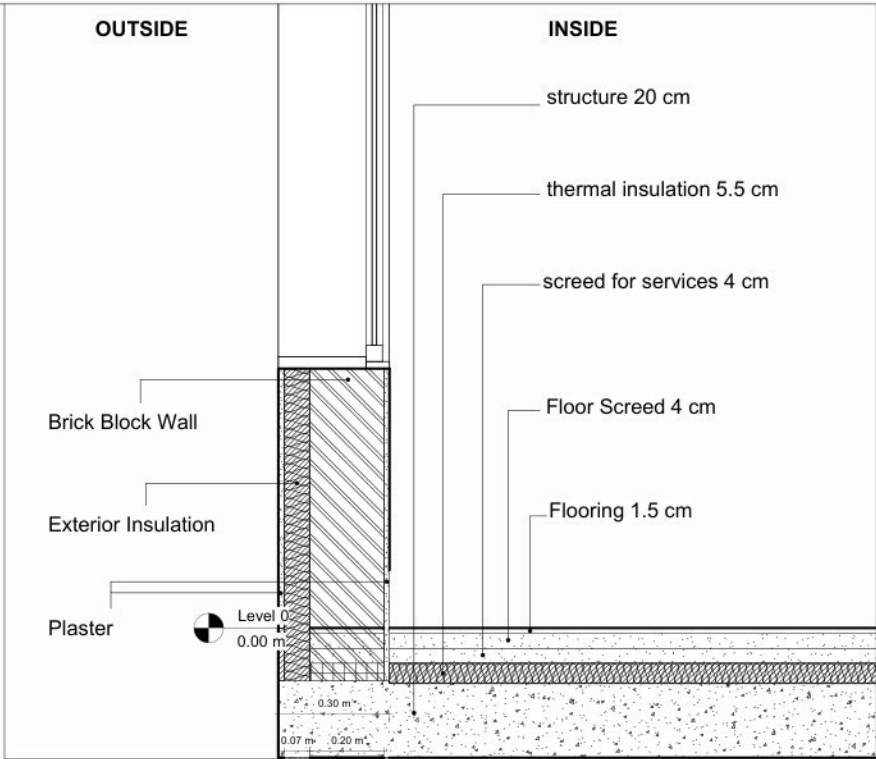

GROUND FLOOR DETAIL
EXTERNAL WALL SECTION